Avadi Corporation / Municipality

Online Application No : 4HO7C1C2 Generated on: 25/10/2024

PERMIT FOR CONSTRUCTION OF BUILDING BY SELF CERTIFICATION

BUILDING PERMIT/LICENSE NO.			
SWP/SCM/CMDA/CMA/0050701/2024			
Zone	Ward	Date of receipt of application	Date of Approval
AVADI	WD-34	25/10/2024	25/10/2024

A. DETAILS OF APPLICANT		
1	Name of the Owner	Mrs.LAVANYA M
2	Son/Wife/Daughter of	W/o-MANIKANDAN
3	Address for correspondence	NO 45, PILLAIYAR KOVIL STREET, JEEVA NAGAR, , Avadi -Village, Avadi -Taluk, Tiruvallur -District, 600054
4	Mobile Number	9710135777
B. DETAILS OF THE PLOT		
1	Extent of plot in Sq.ft.	1221.00
2	Plot No./Door No.	8
3	SF No./TS No.	85/1B2
4	Name of Street	JEEVA NAGAR,AVADI
5	Ward No. and Block No.	WD-34 -Ward No.
6	Village Name and / or Local Body Name	Paruthipattu -Village, Avadi -LocalBody.

7	Taluk and District	Avadi -Taluk, Tiruvallur -District.			
C. DETAILS OF THE PROPOSED BUILDING					
1	Type of Building Permission (New building/Revision to earlier approved plan/Additional construction)	New			
2	Usage	Residential			
3	Number of Dwelling Units	Ground Floor	First Floor		
		1	0		
4	Floor wise built up area	Ground Floor area (sq.ft)	First Floor area (sq.ft)		
		650.25	895.67		
5	Total Built Up area (in sq.ft)	1545.92			
6	Height of the building (in m)	6.93			
7	Setbacks (in m)	Front	Rear	Side 1	Side 2
		1.56	0.60	1.00	0
D. DETAILS OF PAYMENT					
1	Fees paid (in Rupees)	122077			

Permission is granted to the construction of the aforesaid building, self-certified by the applicant,subject to the following conditions.

1	This Building Permit/License is valid from 25/10/2024 to 25/10/2029 (5 Years).
2	This building permit/license issued does not confer any ownership right of the applicant over the land/plot and cannot be produced as an evidence in proof of the title of the applicant in court of law.
3	If the land/plot under reference falls in Govt. land / Municipal land / open space reservations of approved or regularised layout, lands prohibited for development,lands earmarked for public purpose in the Master Plan, Detailed Development Plan, New Town Development Plan, lands earmarked for roads in the grid of roads plan,waterbodies, CRZ area, HACA and development prohibited/restricted areas in Rule 19 (Annexure XVII) of TNCD&BR, 2019, lands classified as Agriculture, Institution,Special & Hazardous , Non Urban, Open Space and Recreational Use Zone and site falling in street alignment/ road widening, the Building Permit/License will stand cancelled and action will be initiated against the building as per the provisions of the Tamil Nadu Town and Country Planning Act,1971, Tamil Nadu Urban Local Bodies Act, 1998, Tamil Nadu Panchayats Act, 1994.
4	The building shall be constructed in compliance with the rules in Annexure XXIV of TNCD&BR, 2019. If the building is constructed in violation of the rules and the conditions therein, action will be taken against the building as per the provisions of the Tamil Nadu Town and Country Planning Act, 1971, Tamil Nadu Urban Local Bodies Act, 1998, Tamil Nadu Panchayats Act, 1994.
5	Post verification of the details self certified by the applicant and the plan generated will be carried out by the officials as per the rules in Annexure XXIV of the Tamil Nadu Combined Development and Building Rules, 2019.

6	This is a self certified and self generated permit, any fraud or misrepresentation of material facts in contravention of the provisions of the relevant Acts and rules shall make the applicant liable for prosecution and punishment under section 236 of the Bharatiya Nyaya Sanhita, 2023 (Central Act 45 of 2023) and section 379 of the Bharatiya Nagarik Surakhsa Sanhita, 2023 (Central Act 46 of 2023) and any other law applicable thereto for furnishing false information and wrong documents.
7	The structural design of foundations, elements of masonry, timber, plain concrete, reinforced concrete, pre-stressed concrete and structural steel must comply with Rule 51(2) Annexure XI of Tamil Nadu Combined Development and Building Rules, 2019
8	In unsewered areas, septic tank shall be provided as per Rule 54(3)(b) of Tamil Nadu Combined Development and Building Rules, 2019
9	Rainwater harvesting structures must be constructed as per Rule 63(1) of Tamil Nadu Combined Development and Building Rules, 2019 on the premises of the building failing to which the construction shall be deemed as unauthorised and in violation of the rules and relevant action will be initiated.
10	Separate Sump shall be constructed as per Rule 63(2)(c) of Tamil Nadu Combined Development and Building Rules, 2019
11	No construction material/debris should be dumped on the public streets.
12	It is obligatory to file return for assessment of property tax within thirty days from the date of completion of construction or date of occupation whichever is earlier as per rule no.256 and 258 of ULB Rules, 1998.

Applicant Name: Mrs.LAVANYA M

Date : 25/10/2024

Signature valid

Signed by: 9841431533
Location:Tiruvallur
Date:2024.10.25 12:40:53

Note: This is a computer-generated letter and doesn't require any signature of the official.

DIRECTORATE OF MUNICIPAL ADMINISTRATION

PAYMENT RECEIPT

CONSTRUCTION OF BUILDING BY SELF CERTIFICATION

Date : 11/11/2024

Applicant : LAVANYA M

Application No : 4HO7C1C2

Fees Type : Selfcertification Fees

Receipt : 2024111150701

Transaction ID : 5738099

Payment Splitup


S.No	Description	Amount
1	Selfcertification Fees	122077
2	Regularization charges	-
3	Development charges	-
4	Labour Fund charges	-
	Total Fees	122077

Amount In Words : Rupees One Lakh Twenty Two Thousand Seventy Seven Only

With Regards,
CMA


OWNER : Mrs. M. LAVANYA.

PLOT REGULARISATION PERMIT No.148/2024/F2,
ROC NO: 1879/2024/F2, DATED- 03.06.2024

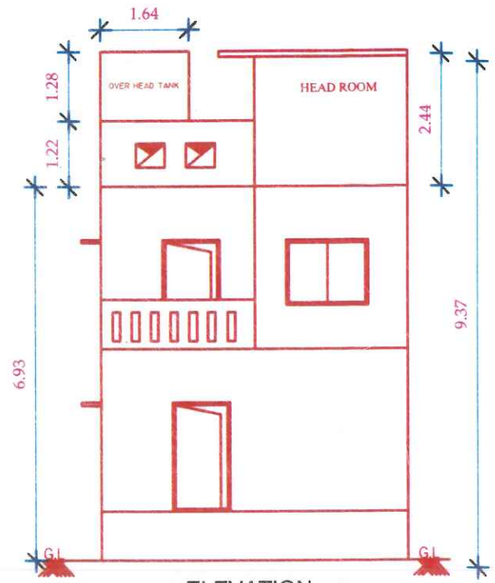


ELEVATION

(SCALE 1:100)

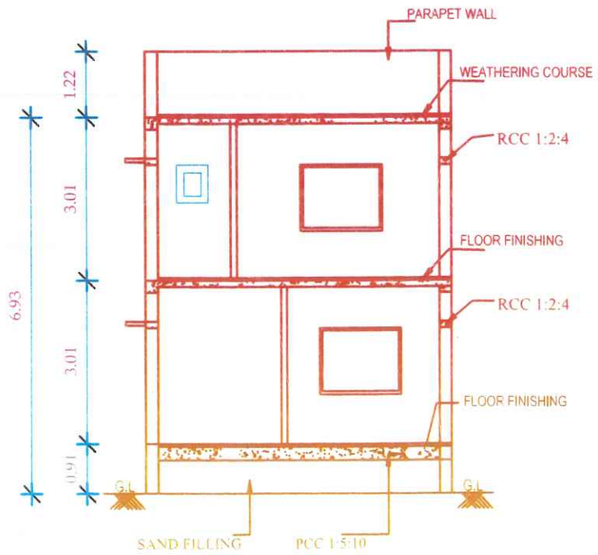


SECTION -XX

(SCALE 1:100)

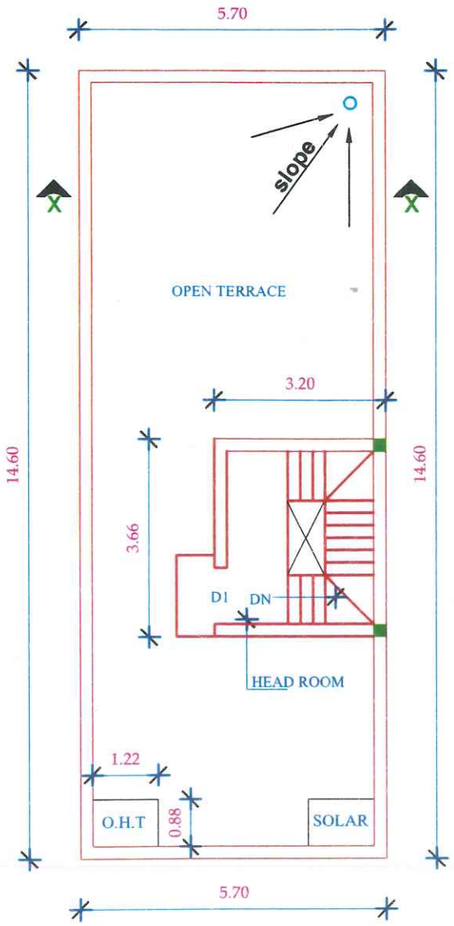

OPEN TERRACE FLOOR PLAN

(SCALE 1:100)

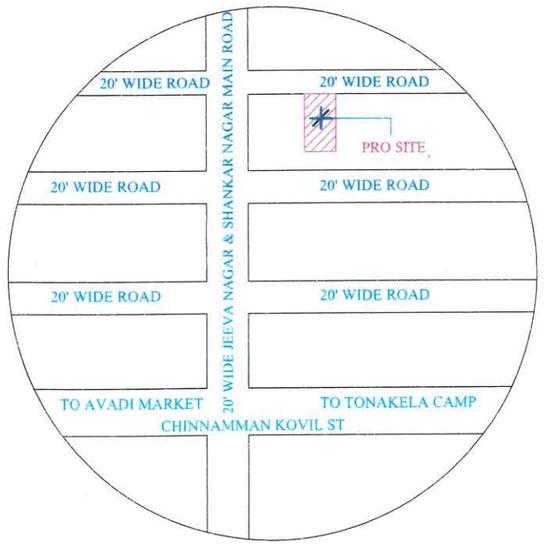

KEY PLAN [N.T.S]

SHEET NO: 02 / 02

PLAN SHOWING THE PROPOSED NEW CONSTRUCTION OF A RESIDENTIAL BUILDING AT PLOT NO: 8, IN S.NO.85/1B2,"JEEVA NAGAR" (T.S.NO: 6/16, BLOCK NO: 37, WARD: I), PARUTHIPATTU VILLAGE, AVADI TALUK, THIRUVALLUR DISTRICT, AVADI CITY MUNICIPAL CORPORATION LIMIT.

NOTE : ALL DIMENSIONS ARE IN METRE

AREA STATEMENT DETAILS

SITE AREA : 113.47 SQ.M / 1221.00 SQ.FT

SPECIFICATION :

FOUNDATION : RCC 1:11/2:3 M25 Concrete Column footing Laid over sand filling and PCC 1:4:8.

RCC WORK : All Column, Beams, Roof Slab, Lintel, Sunshade are in CC 1:5.5:3 (M-25)

BRICKWORK : B.W in Basement Superstructure are in CM 1:5.

JOINERY : Joineries are made with Steel (or) first class teak wood.

WEATHERING COURSE : 9" x 9" Pressed Tiles laid over the Brick Jelly with Lime mortar and sloped with water proofing compound.

PLASTERING : Ceiling plastering with CM 1:3
Inside & Outside walls are plastering with CM 1:4.

PAINTING : White washing with two coats over the one coat of primer for Ceiling.Colour washing washing with two coats over one coat of primer for all Walls.

INDEX :

SITE BOUNDARY

PROPOSED BUILDING

EXISTING ROAD

REFERENCE :

SCALE : 1:100

DATE : 25 OCT 2024

N
W E
S

ARCHITECT / REGISTERED ENGINEER :

V.ARUN PANDIAN M.E.
CMDA REGISTERED Reg.No-SE/GR/II/079
Avadi City Municipal Corporation
Reg.No- 09 / 2019
Structural Engineer (Grade -II)
No.[illegible] Chennai-54.
Cell-9840[illegible]06


Signature valid
Signed by: 9841[illegible]33
Location: Tiruvallur
Date:2024.[illegible]12:59:15

APPLICANT :


OWNER : Mrs. M. LAVANYA.

PLOT REGULARISATION PERMIT No.148/2024/F2,
ROC NO: 1879/2024/F2, DATED- 03.06.2024

PLOT NO: 11

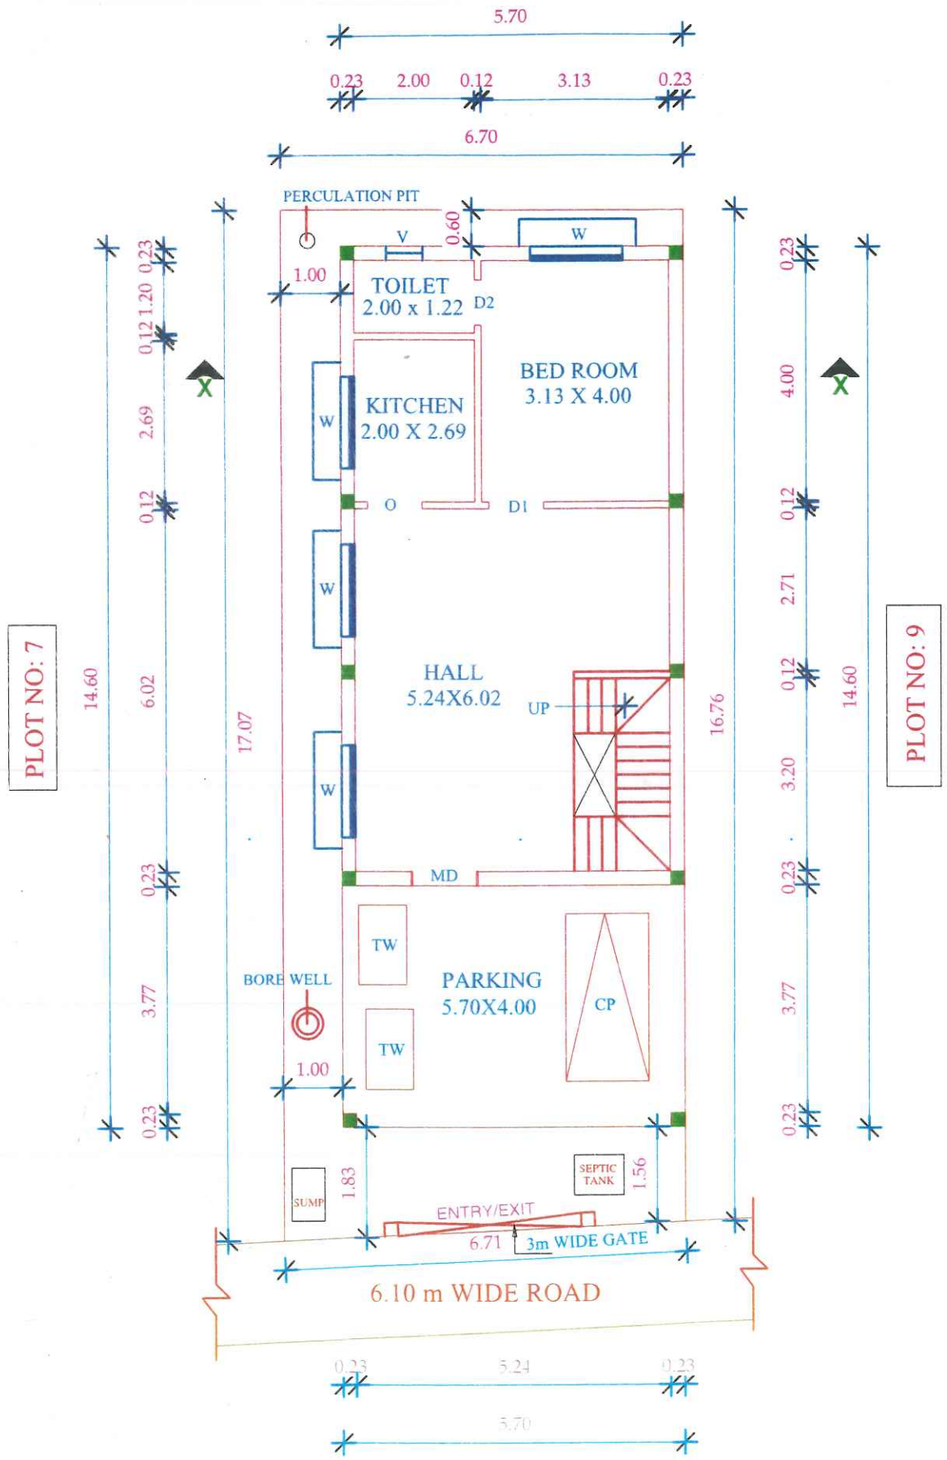

SITE CUM GROUND FLOOR PLAN
(SCALE 1:100)

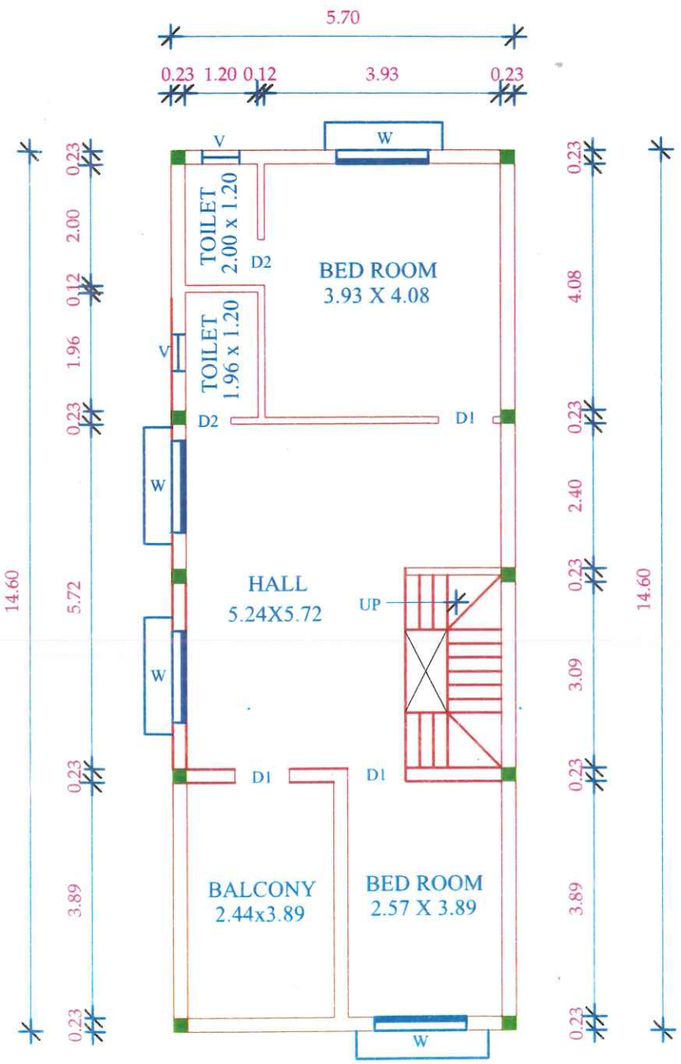

FIRST FLOOR PLAN
(SCALE 1:100)

SHEET NO: 01 / 02

PLAN SHOWING THE PROPOSED NEW CONSTRUCTION OF A RESIDENTIAL BUILDING AT PLOT NO: 8,IN S.NO.85/1B2,"JEEVA NAGAR" (T.S.NO: 6/16, BLOCK NO: 37, WARD: I), PARUTHIPATTU VILLAGE, AVADI TALUK, THIRUVALLUR DISTRICT, AVADI CITY MUNICIPAL CORPORATION LIMIT.

NOTE : ALL DIMENSIONS ARE IN METRE

AREA STATEMENT DETAILS

SITE AREA : 113.47 SQ.M / 1221.00 SQ.FT

PROPOSED RESIDENTIAL BUILDING AREA DETAILS :

S.NO	DESCRIPTION	FSI (SQ.M)	NON-FSI (SQ.M)	TOTAL (SQ.M)
01	GROUND FLOOR	60.41	22.80	83.21
	FIRST FLOOR	83.21	-	83.21
	HEAD ROOM AREA	-	11.69	11.69
	TOTAL AREA	143.62	34.49	178.11

TOTAL FSI AREA = 143.62 SQ.M

FLOOR SPACE INDEX = $\frac{143.62}{113.43}$ = 1.26

JOINERY SCHEDULE

MD	1.20 x 2.10	MAIN DOOR
D	0.90 x 2.10	DOOR
D1	0.75 x 2.10	DOOR
W	1.20 X 1.20	WINDOW
W1	1.80 X 1.50	WINDOW
KW	1.80 X 1.20	WINDOW
V	0.60 x 0.60	VENTILATOR

INDEX :
SITE BOUNDARY
PROPOSED BUILDING
EXISTING ROAD

REFERENCE :
SCALE : 1:100
DATE : 25 OCT 2024

S E W N

ARCHITECT / REGISTERED ENGINEER

DWELLING UNIT DETAILS :

DWELLING UNIT -01	143.62 SQ.M

V.ARUN PANDIAN M.E.
CMDA REGISTERED Reg.No-SE/GR/II/079
Avadi City Municipal Corporation
Reg.No- 09 / 2019
Structural Engineer (Grade -II)
No-243,N.M ROAD,AVADI.Chennai-54.
Cell-9840470606.